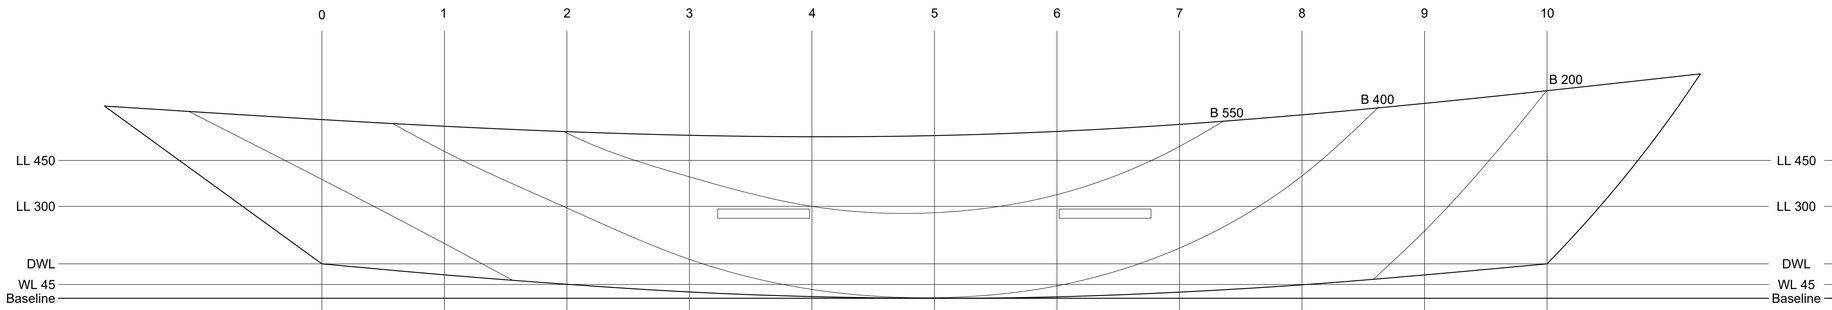

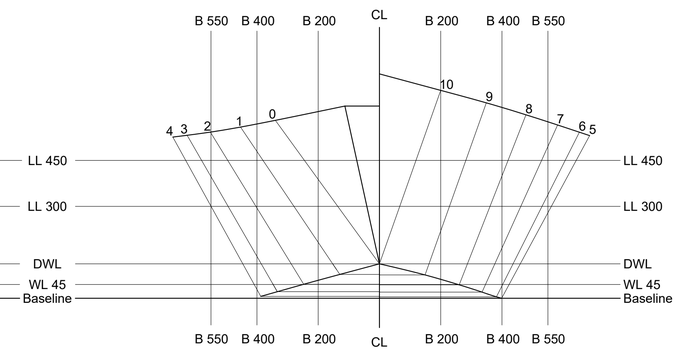

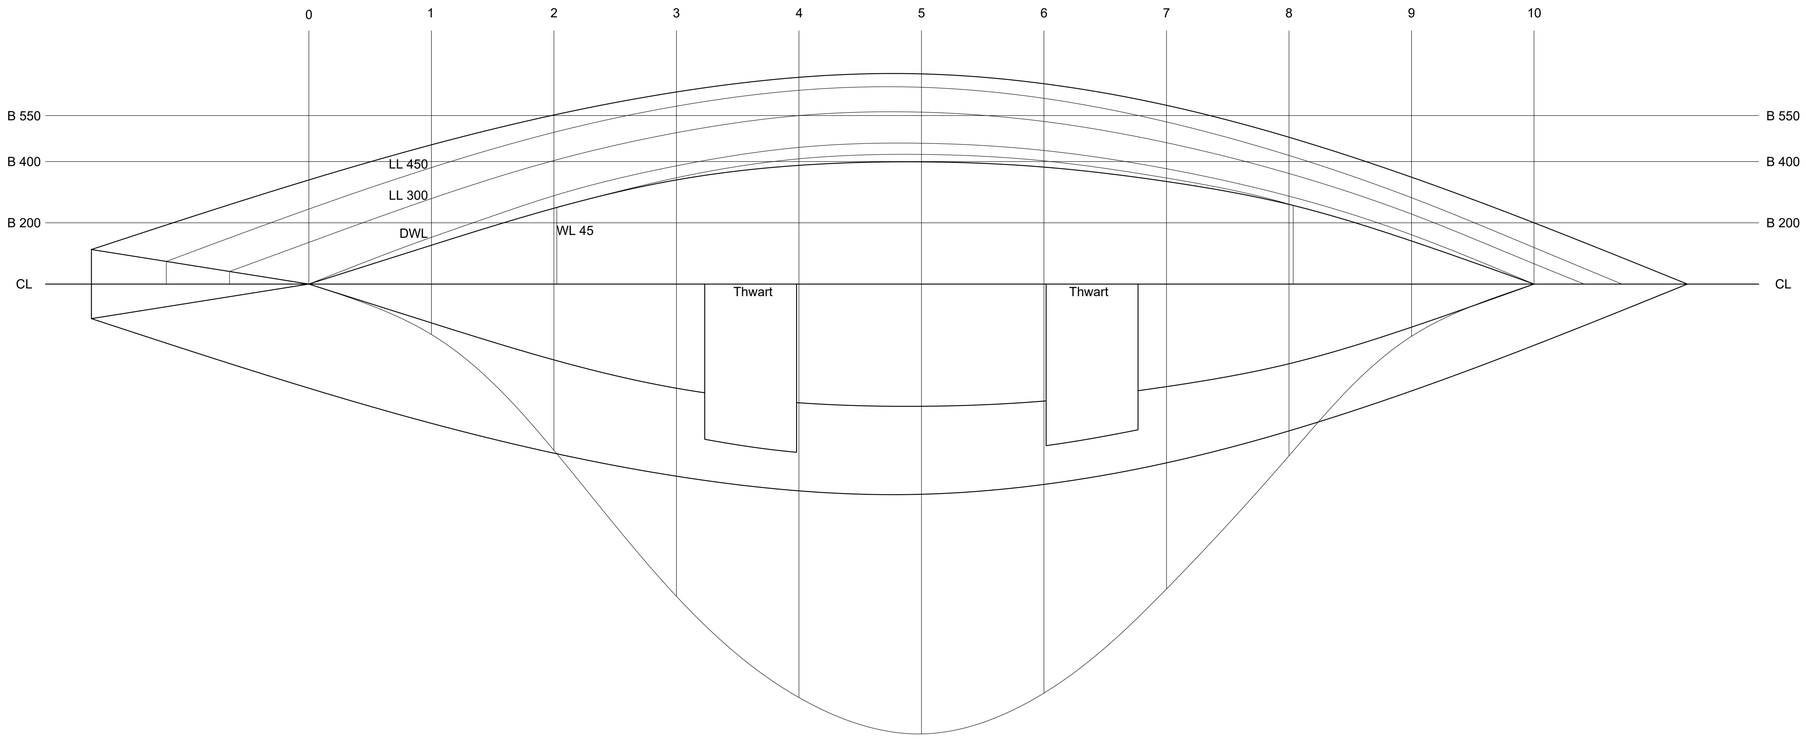

Parameters	Values	Unit
LOA	5.21	m
LWL	4	m
ΔD	200	kg
∇D	0.195	m^3
Station spacing	0.4	m
A max	0.095	m^2
Chine Bmax	0.08	m
BWL	0.092	m
BOA	0.138	m
VCB	0.045	m
LCB	0	m from Mid
LCF	0	m from Mid
GM	0.06	m from BL
Tc Max	0.11	m
Cp	0.5	N/A
Cb	0.49	N/A
Cm	0.987	N/A
Cw	0. 70	N/A
TPC SW	0.0233	tonnes/cm
TPC FW	0.0227	tonnes/cm

SOLENT UNIVERSITY

Issue date: 9/12/25	Scale: 1:10	File name: Dory Linesplan Final.dwg
Drawn by: Q103050818	Units: mm	Projection method: N/A
Drawing number: 004		**Drawing title: Dory Linesplan Final**
Edition: 001	Sheet: 1 of 1	

Designed and produced by Steve Crook ©